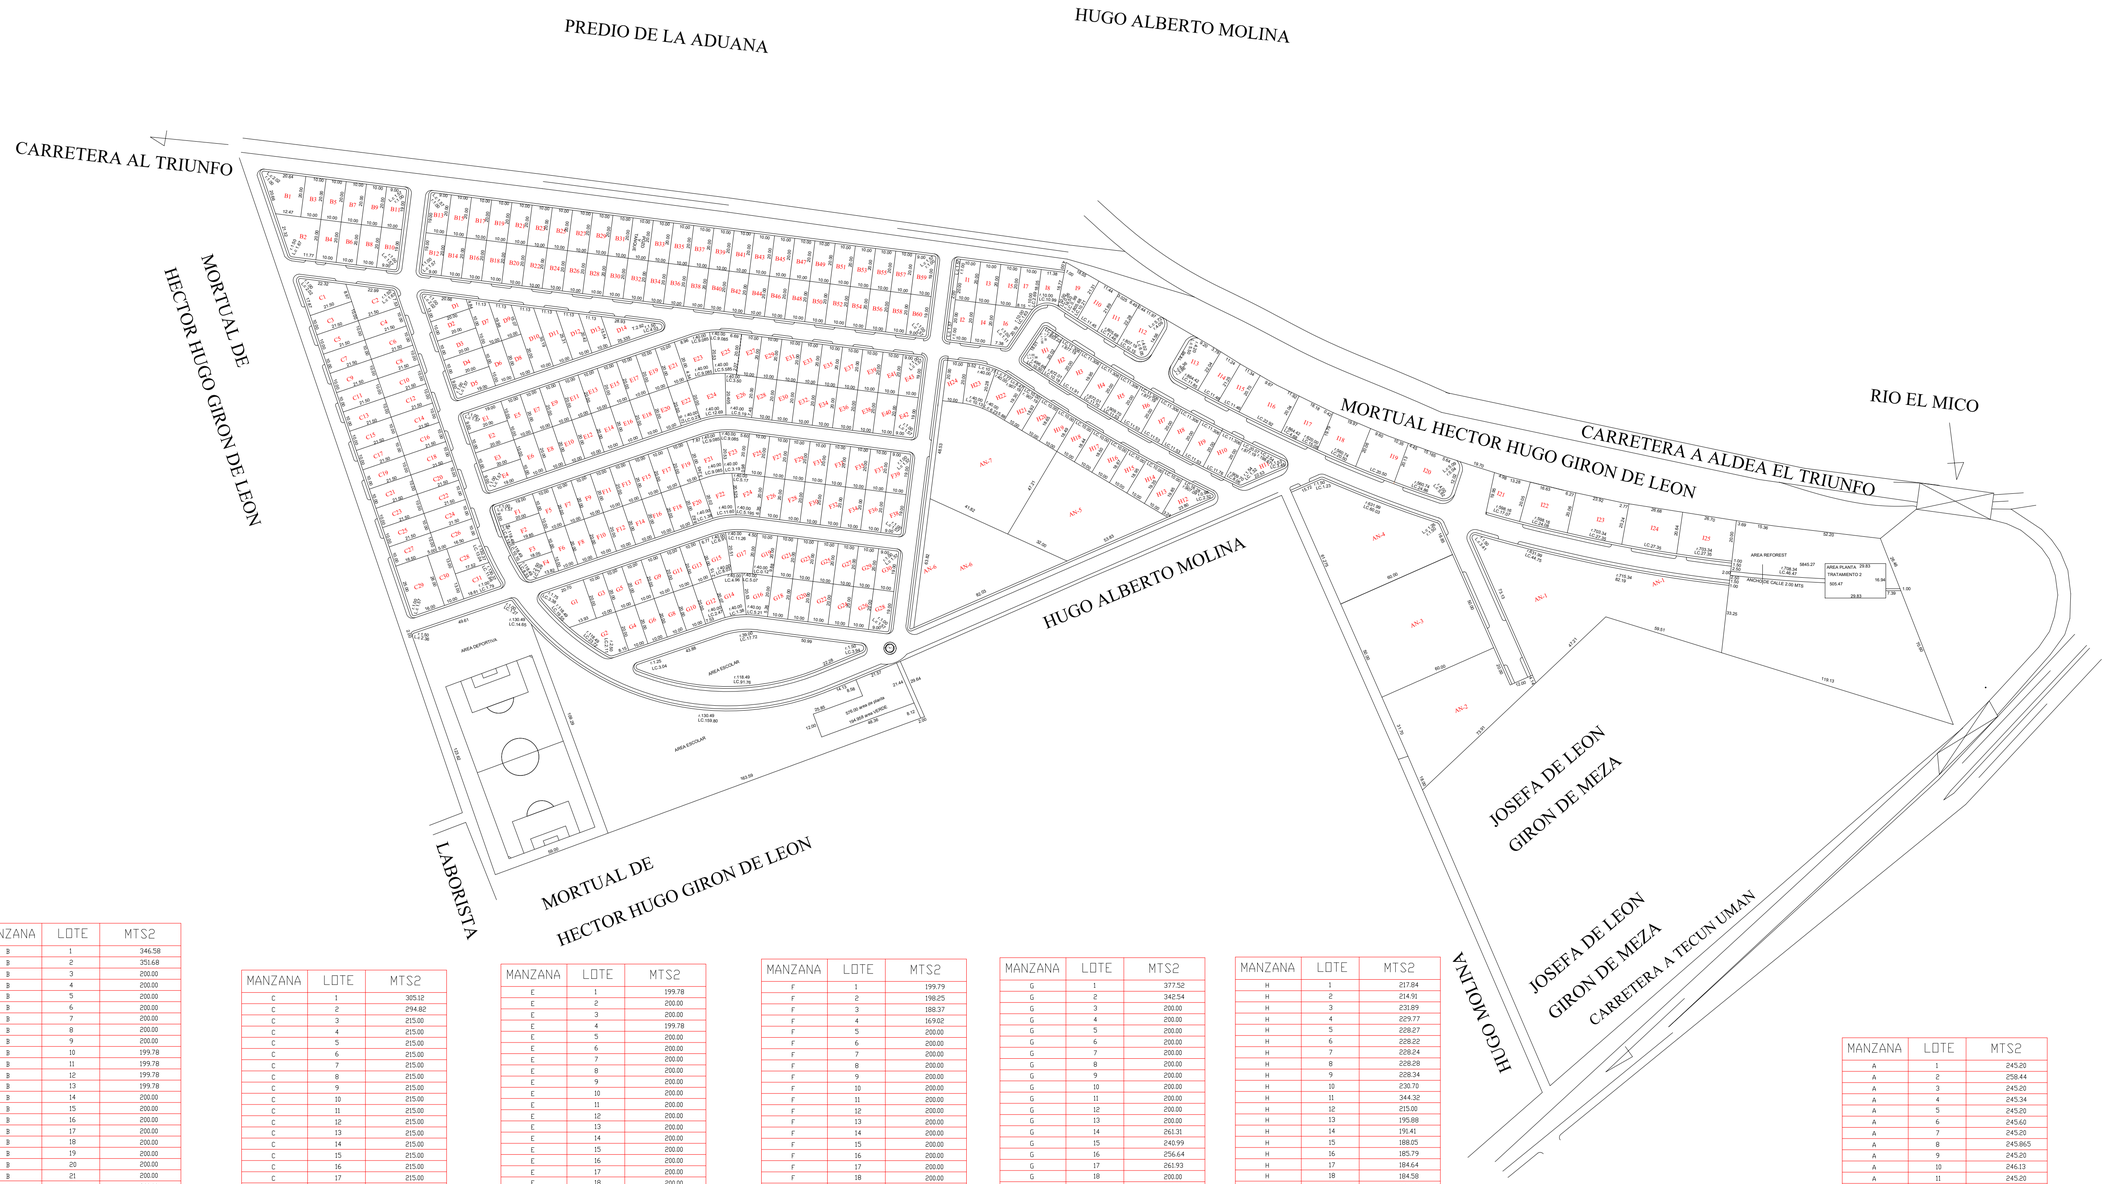

MANZANA	LOTE	MTS2
B	1	346.58
B	2	351.68
B	3	200.00
B	4	200.00
B	5	200.00
B	6	200.00
B	7	200.00
B	8	200.00
B	9	200.00
B	10	199.78
B	11	199.78
B	12	199.78
B	13	199.78
B	14	200.00
B	15	200.00
B	16	200.00
B	17	200.00
B	18	200.00
B	19	200.00
B	20	200.00
B	21	200.00
B	22	200.00
B	23	200.00
B	24	200.00
B	25	200.00
B	26	200.00
B	27	200.00
B	28	200.00
B	29	200.00
B	30	200.00
B	31	200.00
B	32	200.00
B	33	200.00
B	34	200.00
B	35	200.00
B	36	200.00
B	37	200.00
B	38	200.00
B	39	200.00
B	40	200.00
B	41	200.00
B	42	200.00
B	43	200.00
B	44	200.00
B	45	200.00
B	46	200.00
B	47	200.00
B	48	200.00
B	49	200.00
B	50	200.00
B	51	200.00
B	52	200.00
B	53	200.00
B	54	200.00
B	55	200.00
B	56	200.00
B	57	200.00
B	58	200.00
B	59	199.78
B	60	199.78

MANZANA	LOTE	MTS2
C	1	305.12
C	2	294.82
C	3	215.00
C	4	215.00
C	5	215.00
C	6	215.00
C	7	215.00
C	8	215.00
C	9	215.00
C	10	215.00
C	11	215.00
C	12	215.00
C	13	215.00
C	14	215.00
C	15	215.00
C	16	215.00
C	17	215.00
C	18	215.00
C	19	215.00
C	20	215.00
C	21	215.00
C	22	215.00
C	23	215.00
C	24	215.00
C	25	215.00
C	26	215.00
C	27	215.00
C	28	219.69
C	29	428.78
C	30	260.00
C	31	241.05

MANZANA	LOTE	MTS2
D	1	193.93
D	2	200.00
D	3	200.00
D	4	200.00
D	5	199.78
D	6	200.00
D	7	824.01
D	8	200.00
D	9	175.17
D	10	326.34
D	11	277.50
D	12	228.67
D	13	179.84
D	14	240.60

MANZANA	LOTE	MTS2
E	1	199.78
E	2	200.00
E	3	200.00
E	4	199.78
E	5	200.00
E	6	200.00
E	7	200.00
E	8	200.00
E	9	200.00
E	10	200.00
E	11	200.00
E	12	200.00
E	13	200.00
E	14	200.00
E	15	200.00
E	16	200.00
E	17	200.00
E	18	200.00
E	19	200.00
E	20	200.00
E	21	200.00
E	22	200.00
E	23	317.92
E	24	322.50
E	25	272.54
E	26	283.06
E	27	200.00
E	28	200.00
E	29	200.00
E	30	200.00
E	31	200.00
E	32	200.00
E	33	200.00
E	34	200.00
E	35	200.00
E	36	200.00
E	37	200.00
E	38	200.00
E	39	200.00
E	40	200.00
E	41	200.00
E	42	199.78
E	43	199.78

MANZANA	LOTE	MTS2
F	1	199.79
F	2	198.25
F	3	188.37
F	4	169.02
F	5	200.00
F	6	200.00
F	7	200.00
F	8	200.00
F	9	200.00
F	10	200.00
F	11	200.00
F	12	200.00
F	13	200.00
F	14	200.00
F	15	200.00
F	16	200.00
F	17	200.00
F	18	200.00
F	19	200.00
F	20	200.00
F	21	296.03
F	22	283.53
F	23	250.66
F	24	278.24
F	25	200.00
F	26	200.00
F	27	200.00
F	28	200.00
F	29	200.00
F	30	200.00
F	31	200.00
F	32	200.00
F	33	200.00
F	34	200.00
F	35	200.00
F	36	200.00
F	37	200.00
F	38	199.78
F	39	199.78

MANZANA	LOTE	MTS2
G	1	377.52
G	2	342.54
G	3	200.00
G	4	200.00
G	5	200.00
G	6	200.00
G	7	200.00
G	8	200.00
G	9	200.00
G	10	200.00
G	11	200.00
G	12	200.00
G	13	200.00
G	14	261.31
G	15	240.99
G	16	256.64
G	17	261.93
G	18	200.00
G	19	200.00
G	20	200.00
G	21	200.00
G	22	200.00
G	23	200.00
G	24	200.00
G	25	200.00
G	26	200.00
G	27	200.00
G	28	199.78
G	29	200.00
G	30	199.78

MANZANA	LOTE	MTS2
H	1	217.84
H	2	214.91
H	3	231.89
H	4	229.77
H	5	228.27
H	6	228.22
H	7	228.24
H	8	228.28
H	9	228.34
H	10	230.70
H	11	344.32
H	12	215.00
H	13	195.88
H	14	191.41
H	15	188.05
H	16	185.79
H	17	184.64
H	18	184.58
H	19	185.63
H	20	187.78
H	21	190.90
H	22	279.46
H	23	246.67
H	24	200.00

MANZANA	LOTE	MTS2
I	1	200.00
I	2	200.00
I	3	200.00
I	4	200.00
I	5	200.00
I	6	260.00
I	7	198.04
I	8	178.43
I	9	312.99
I	10	247.24
I	11	253.78
I	12	352.07
I	13	351.79
I	14	245.71
I	15	239.02
I	16	449.96
I	17	381.54
I	18	404.49
I	19	405.20
I	20	560.68
I	21	351.31
I	22	476.27
I	23	545.10
I	24	554.65
I	25	551.39

MANZANA	LOTE	MTS2
A	1	245.20
A	2	258.44
A	3	245.20
A	4	245.34
A	5	245.20
A	6	245.60
A	7	245.20
A	8	245.865
A	9	245.20
A	10	246.13
A	11	245.20
A	12	246.39
A	13	245.20
A	14	246.65
A	15	245.20
A	16	246.91
A	17	245.20
A	18	247.17
A	19	245.20
A	20	247.43
A	21	245.20
A	22	247.70
A	23	245.20
A	24	247.96
A	25	245.20
A	26	248.22
A	27	268.26
A	28	248.48
A	29	308.12
A	30	248.74
A	31	279.71
A	32	332.13

EMPRESA:
PROYECTO: URBANIZACION
CONSTRUYE:

PLANO DE: DISTRIBUCION Y NUMERACION DE LOTES
TELEFONOS

DIBUJO:
CALCULO:
ESCALA: 1:1500 HOJA No.
FECHA: 17 NOVIEMBRE 2005 DE:
Vo. Bo.

DIRECCION:
COLONIA:
MUNICIPIO: AYUTLA
DEPARTAMENTO: SAN MARCOS
Vo. Bo.